

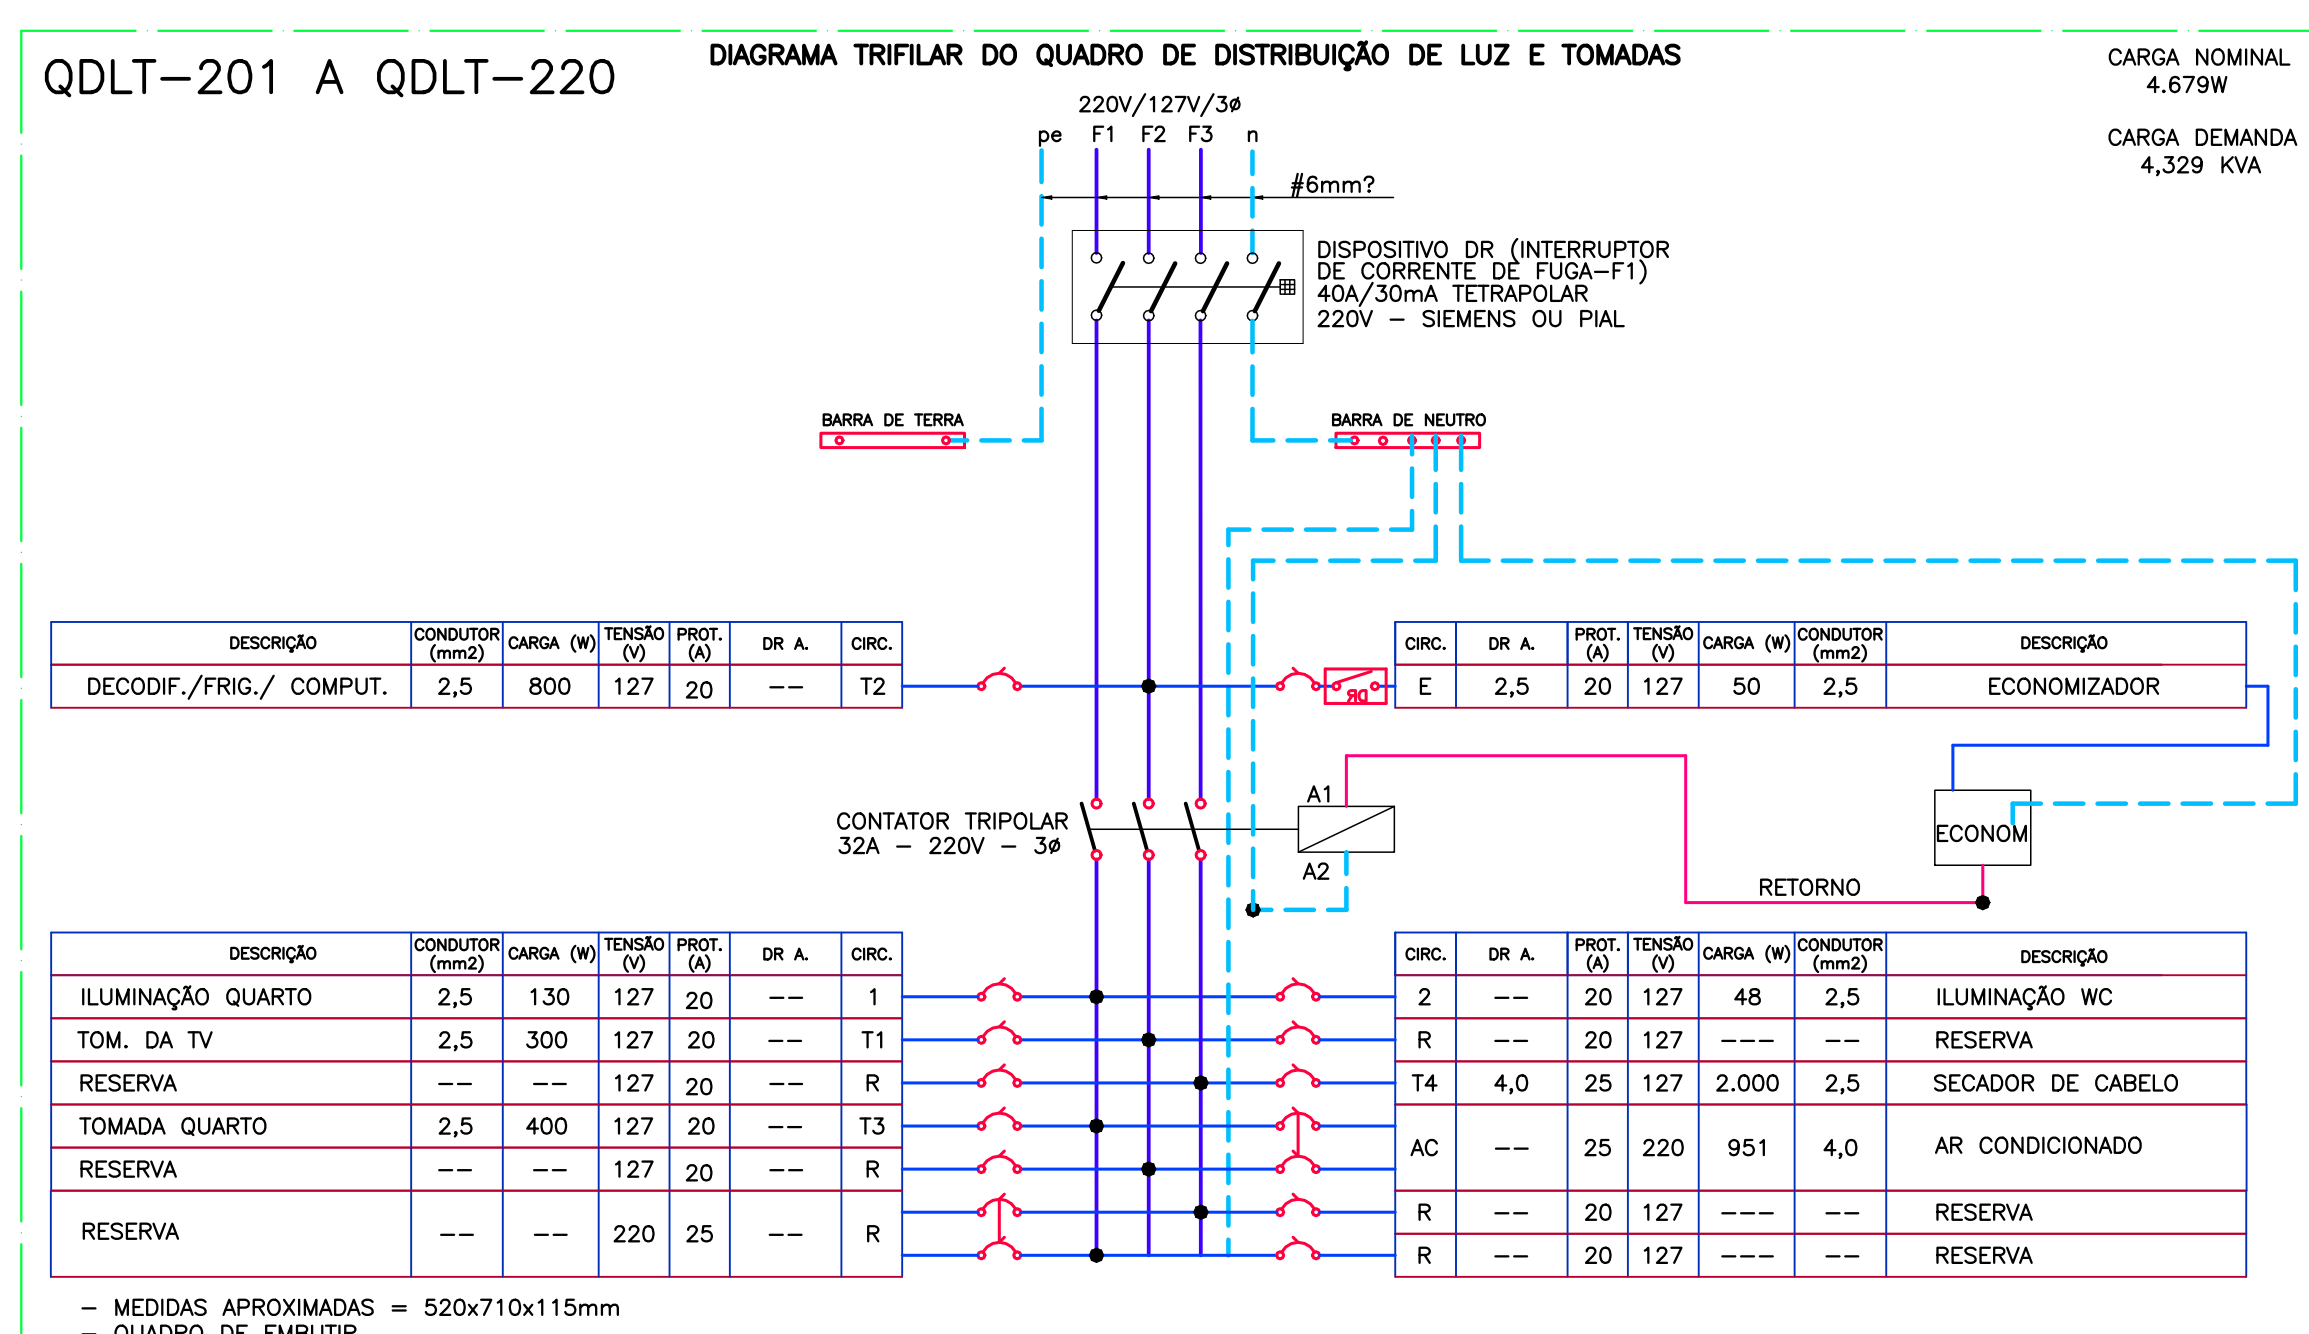


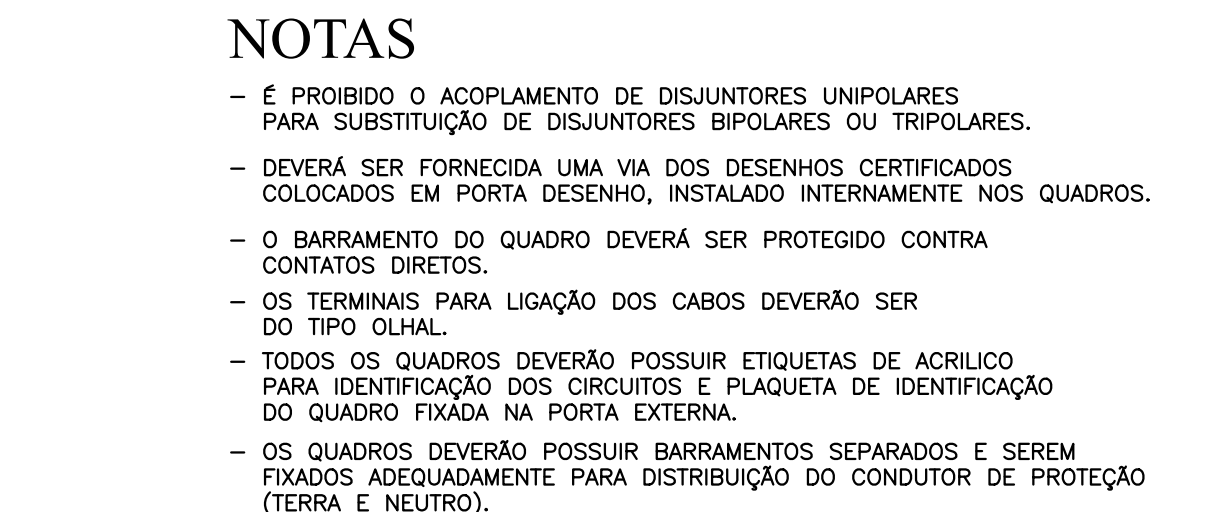

ANÁLISE DE CARGAS DOS QUADROS: DBT-201 AO 220																	
Nº CIRC.	FINALIDADE	QUANT.	CARGA UNIT. (W)	CARGA TOTAL (W)	FATOR POTENCIA	CARGA TOTAL (VA)	FATOR DEMANDA	CARGA DEMANDA (VA)	TENSÃO (V)	CORRENTE (A)	DISJUNTOR (A)	FAÇAÇÃO	FASE (VA)	R FASE (VA)	S FASE (VA)		
BARRAMENTO PRINCIPAL																	
1	ILUMINAÇÃO QUARTO	8	3	9,5	18	130	1,00	130	0,75	98	127	1	1,02	0,5	2,5		
2	ILUMINAÇÃO WC	5	15	18	48	100	1,00	48	0,75	36	127	1	0,37	0,5	2,5		
3	TV	1	300	300	300	0,75	225	127	1	1,35	127	1	1,35	0,5	2,5		
4	TV	2	1	100	600	800	0,75	600	127	1	6,30	0,5	2,5		800,00		
5	TELA	4	100	400	400	0,75	300	127	1	3,75	127	1	3,75	0,5	2,5		
6	DECODEADOR DE CABELO	1	2.000	2.000	2.000	1,00	2.000	127	1	15,75	25				2.000,00		
7	E ECONOMIZADOR	1	50	50	50	0,75	38	127	1	0,39	20	0,5	2,5	50,00			
8	AR CONDICIONADO	1	951	951	1.034	1,00	1.034	127	1	9,82	20	0,5	40	475,00	475,50		
9	R RESERVA	0	0	0	0	1,00	0	200	1	0,00	20	0,5					
10	R RESERVA	0	0	0	0	1,00	0	200	1	0,00	20	0,5					
11	R RESERVA	0	0	0	0	1,00	0	200	1	0,00	20	0,5					
12	R RESERVA	0	0	0	0	1,00	0	200	1	0,00	20	0,5					
TOTAL (W)				4.879	TOTAL (VA)	4.763	TOTAL (VA)	4.329	20	13,36	FASES				1.550,0	1.575,5	2.000,0
PR-CAB-CABO-F-Sistema PR-CAB-CABO-F-Sistema PR-CAB-CABO-F-Sistema																	

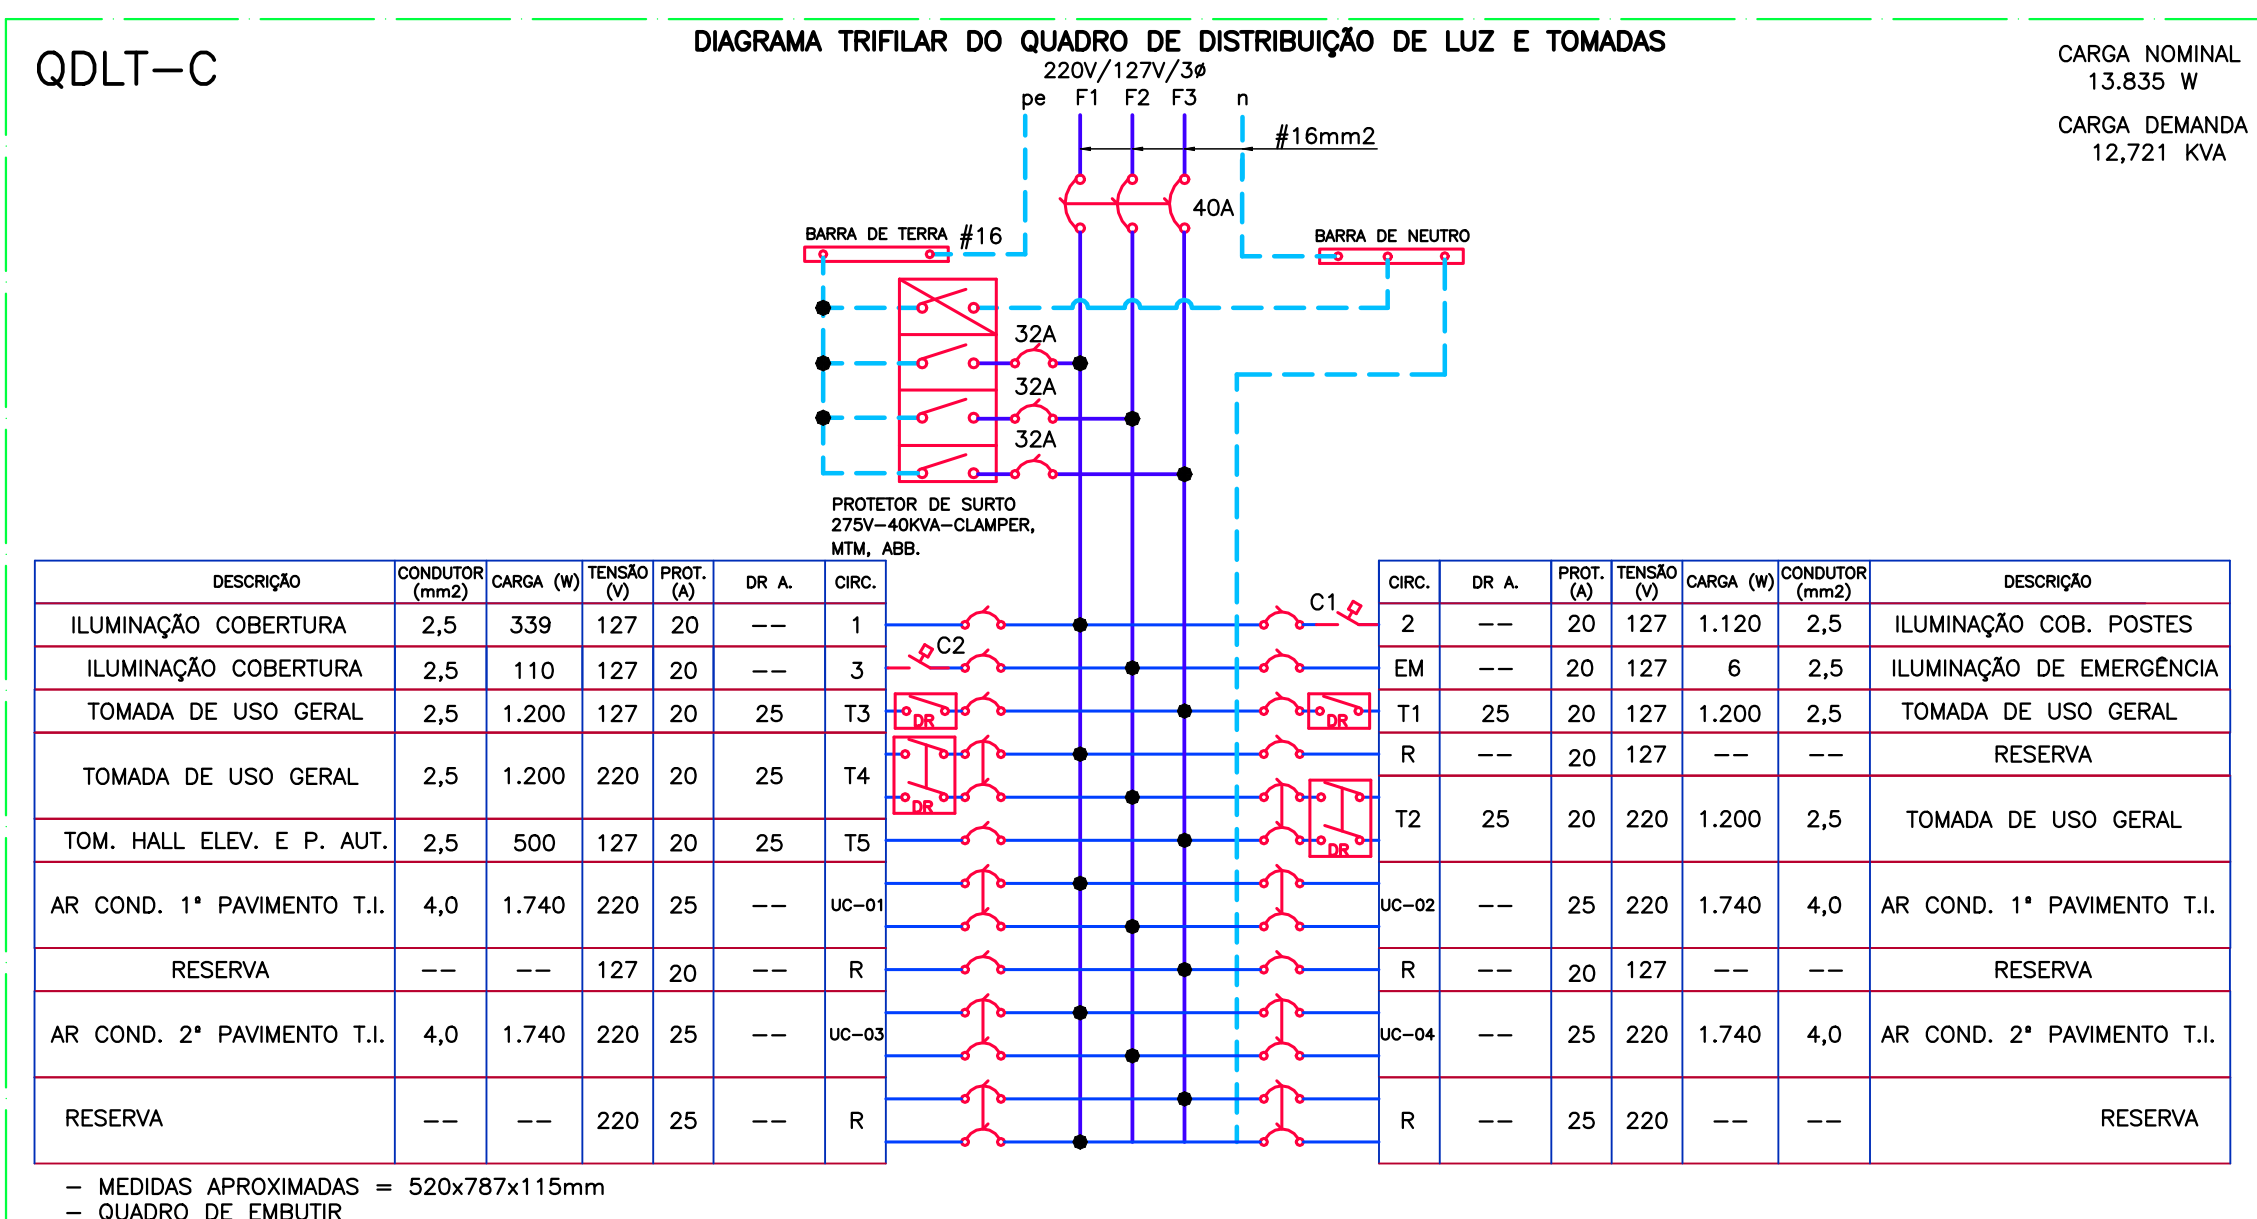

DETALHAMENTO DE CARGAS DOS QUADROS QD-1-C																		
Nº REC.	FINALIDADE	QUANT.		CARGA UNIT. (W)		CARGA TOTAL (W)	FATOR POTENCIA	CARGA TOTAL (VA)	FATOR DEMANDA	CARGA DEMANDA (VA)	TENSÃO (V)	Nº DE FASES	CORRENTE (A)	DISSIPATOR (VA)	FAÇO (A)	FASE (A)	CONDUTOR (mm²)	FASE (V)
BARRAMENTO PRINCIPAL																		
1	ILUMINAÇÃO COBERTURA	12	25	9,5	15	339	1,00	339	0,75	254	127	1	2,67	20	0,5	2,5	339,00	
2	ILUMINAÇÃO COBERTURA COBERTOS	48				1.100	0,75	825	0,75	619	127	3	8,63	20	0,5	2,5	1.100,00	1.100/0
3	ILUMINAÇÃO COBERTURA	32	50			110	1,00	110	0,75	83	127	1	0,87	20	0,5	2,5	110,00	
4	ILUMINAÇÃO DE EMERGÊNCIA		2		2	8	1,00	8	0,75	6	127	1	0,05	20	0,5	2,5	600,00	
5	TOMADA DE USO GERAL		1.200			1.200	1,00	1.200	0,75	900	220	2	5,45	20	0,5	2,5	1.200,00	1.200/0
6	TOMADA DE USO GERAL		1.200			1.200	1,00	1.200	0,75	900	220	2	5,45	20	0,5	2,5	600,00	600/0
7	TOMADA DE USO GERAL		600			600	1,00	600	0,75	450	220	2	2,73	20	0,5	2,5	600,00	600/0
8	TOMADA DE USO GERAL		600			600	1,00	600	0,75	450	220	2	2,73	20	0,5	2,5	600,00	600/0
9	TOMADA DE USO GERAL		600			600	1,00	600	0,75	450	220	2	2,73	20	0,5	2,5	600,00	600/0
10	TOMADA HA ELEVADOR COM MOTOR AUTOMÁTICA		1.200			1.200	1,00	1.200	0,75	900	220	2	5,45	20	0,5	2,5	600,00	600/0
11	UC-01 AB CONDICIONADO 3° PAVIMENTO T.1.		1		1	1.740	1,00	1.740	0,82	1.428	1.000	1	7,93	25	0,5	4,0	870,00	870,00
12	UC-01 AB CONDICIONADO 3° PAVIMENTO T.2		1		1	1.740	1,00	1.740	0,82	1.428	1.000	1	7,93	25	0,5	4,0	870,00	870,00
13	UC-01 AB CONDICIONADO 3° PAVIMENTO T.3		1		1	1.740	1,00	1.740	0,82	1.428	1.000	1	7,93	25	0,5	4,0	870,00	870,00
14	UC-01 AB CONDICIONADO 3° PAVIMENTO T.1.		1		1	1.740	1,00	1.740	0,82	1.428	1.000	1	7,93	25	0,5	4,0	870,00	870,00
15	UC-01 AB CONDICIONADO 3° PAVIMENTO T.1.		1		1	1.740	1,00	1.740	0,82	1.428	1.000	1	7,93	25	0,5	4,0	870,00	870,00
16	RESERVA		0		0	0	1,00	0	1,00	0	127	1	0,00	20	0,5	2,5		
17	RESERVA		0		0	0	1,00	0	1,00	0	127	1	0,00	20	0,5	2,5		
18	RESERVA		0		0	0	1,00	0	1,00	0	127	1	0,00	20	0,5	2,5		
19	RESERVA		0		0	0	1,00	0	1,00	0	220	2	0,00	20	0,5	2,5		
TOTAL (W)						13.818	TOTAL (VA)	14.640	TOTAL (VA)	12.221	220	3	31,39	DISSIPADOR CARGA C-2: BARRAMENTO PRINCIPAL				
														FASES	3x50/0	470/0	1.500/0	
														1x250/0 1x250/0 1x250/0 1x250/0				

TODOS OS DIREITOS RESERVADOS LEI : 5988/1973

ASSUNTO	INSTALAÇÕES ELÉTRICAS	PROJETO Nº	EL-18-004
---------	-----------------------	------------	-----------

TÍTULO	DIAGRAMAS E TABELAS DE CARGAS
--------	-------------------------------

PROJ.	PAULO	ARQ.	AFESP PERUIBE R02	EMIÇÃO	23/11/2023	ESCALA	1:50	FOLHA	14/14
-------	-------	------	-------------------	--------	------------	--------	------	-------	-------

[illegible]

ESC. DE PLOTAGEM		
1000:50		
COR	PENA	ESPRESSO
1	7	0.25
2	7	0.2
3	7	0.3
4	7	0.4
5	7	0.5
9	7	0.2
10	10	0.2
12	12	0.5
22	22	0.3
100	100	0.3
104	104	0.5
130	130	0.4
140	140	0.4
160	160	0.4
170	170	0.6
180	180	0.5
200	200	0.5
202	202	0.4
230	230	0.4
240	240	0.5